'SKANDA ENCLAVE'

Plan Showing the Proposed Layout of House Sites in S.F.Nos - 265/1B1B, 1B1D2, 1B2, 2A1A, 2B1A & 280/1B1, Pooluvapatti Village, Perur Taluk, Coimbatore District.

Scale:- 1" = 33' (1 : 400).

(DTCP Approved No - 321/2024)

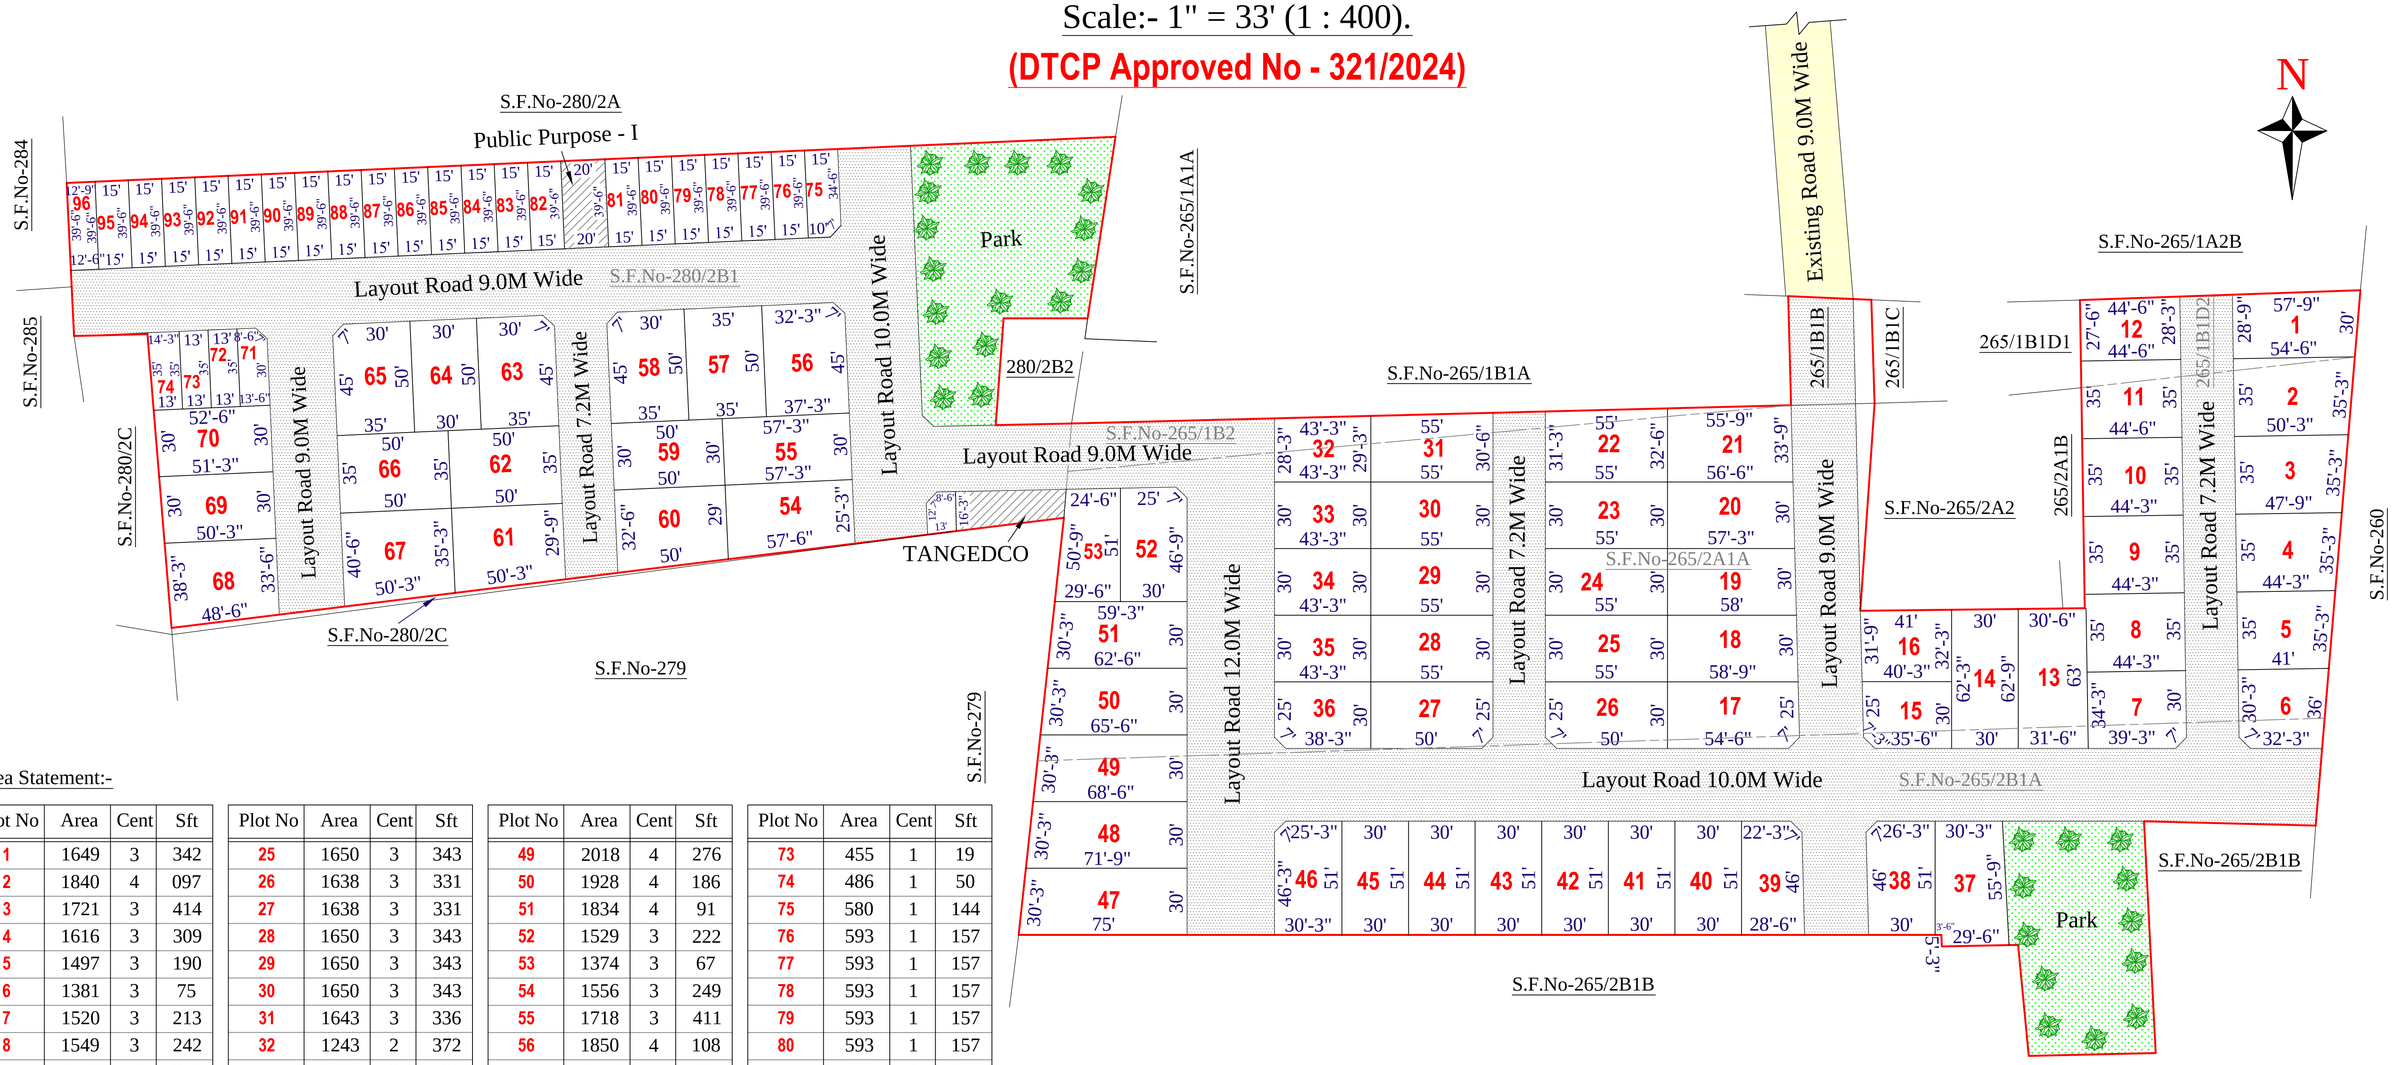

Area Statement:-

Plot No	Area	Cent	Sft
1	1649	3	342
2	1840	4	097
3	1721	3	414
4	1616	3	309
5	1497	3	190
6	1381	3	75
7	1520	3	213
8	1549	3	242
9	1549	3	242
10	1553	3	246
11	1558	3	251
12	1240	2	369
13	1949	4	207
14	1875	4	133
15	1199	2	328
16	1300	2	429
17	1761	4	19
18	1751	4	9
19	1729	3	422
20	1706	3	399
21	1859	4	117
22	1753	4	11
23	1650	3	343
24	1650	3	343

Plot No	Area	Cent	Sft
25	1650	3	343
26	1638	3	331
27	1638	3	331
28	1650	3	343
29	1650	3	343
30	1650	3	343
31	1643	3	336
32	1243	2	372
33	1298	2	426
34	1298	2	426
35	1298	2	426
36	1285	2	414
37	1764	4	22
38	1549	3	243
39	1409	3	102
40	1530	3	223
41	1530	3	223
42	1530	3	223
43	1530	3	223
44	1530	3	223
45	1530	3	223
46	1534	3	227
47	2210	5	32
48	2113	4	370

Plot No	Area	Cent	Sft
49	2018	4	276
50	1928	4	186
51	1834	4	91
52	1529	3	222
53	1374	3	67
54	1556	3	249
55	1718	3	411
56	1850	4	108
57	1750	4	8
58	1738	3	431
59	1500	3	193
60	1538	3	231
61	1629	3	322
62	1750	4	8
63	1738	3	431
64	1500	3	193
65	1738	3	431
66	1750	4	8
67	1898	4	156
68	1771	4	29
69	1523	3	216
70	1556	3	249
71	460	1	24
72	455	1	19

Plot No	Area	Cent	Sft
73	455	1	19
74	486	1	50
75	580	1	144
76	593	1	157
77	593	1	157
78	593	1	157
79	593	1	157
80	593	1	157
81	593	1	157
82	593	1	157
83	593	1	157
84	593	1	157
85	593	1	157
86	593	1	157
87	593	1	157
88	593	1	157
89	593	1	157
90	593	1	157
91	593	1	157
92	593	1	157
93	593	1	157
94	593	1	157
95	593	1	157
96	499	1	63
Total	128521	295	19